




BOOTH CONCEPT 10' x 10' EXHIBIT	
GENERAL NOTES 1. ALL STRUCTURE IS CONTAINED WITHIN THE 10'-0" x 10'-0" BOOTH FOOTPRINT. NOTHING PROJECTS INTO THE AISLE. 2. MAX. OVERALL HEIGHT: 8'-0" (TOP OF TRIANGLE CANOPY). 3. SIDE FRAMES + HEADER BEAM: 7'-6" HIGH, 6" SQ. POSTS AND BEAMS. 4. TRIANGLE CANOPY: 6'-9" EQUILATERAL, 8" FRAME, 5" TAPERED FASCIA, ON (3) 5" SQ. POSTS. 5. CLEAR HEIGHT UNDER CANOPY: 7'-7". 6. MEMBER SIZES & MATERIALS ARE NOMINAL (CONCEPT). FINAL BY FABRICATOR. 7. EXHIBITOR TO VERIFY HEIGHT AND LINE-OF-SIGHT LIMITS FOR THIS BOOTH TYPE IN THE IAAPA EXPO EXHIBITOR MANUAL. 8. DIMENSIONS GOVERN - DO NOT SCALE.	
PROJECT	IAAPA EXPO - 10' x 10' BOOTH
SHOW	IAAPA EXPO
EXHIBITOR	
BOOTH NO.	
BOOTH SIZE	10'-0" x 10'-0"
DRAWING	BOOTH CONCEPT - PLAN, ELEVATIONS & ISOMETRIC
SCALE	1/2" = 1'-0" (ARCH C 24x18)
DATE	09/22/2026
SHEET	A-1

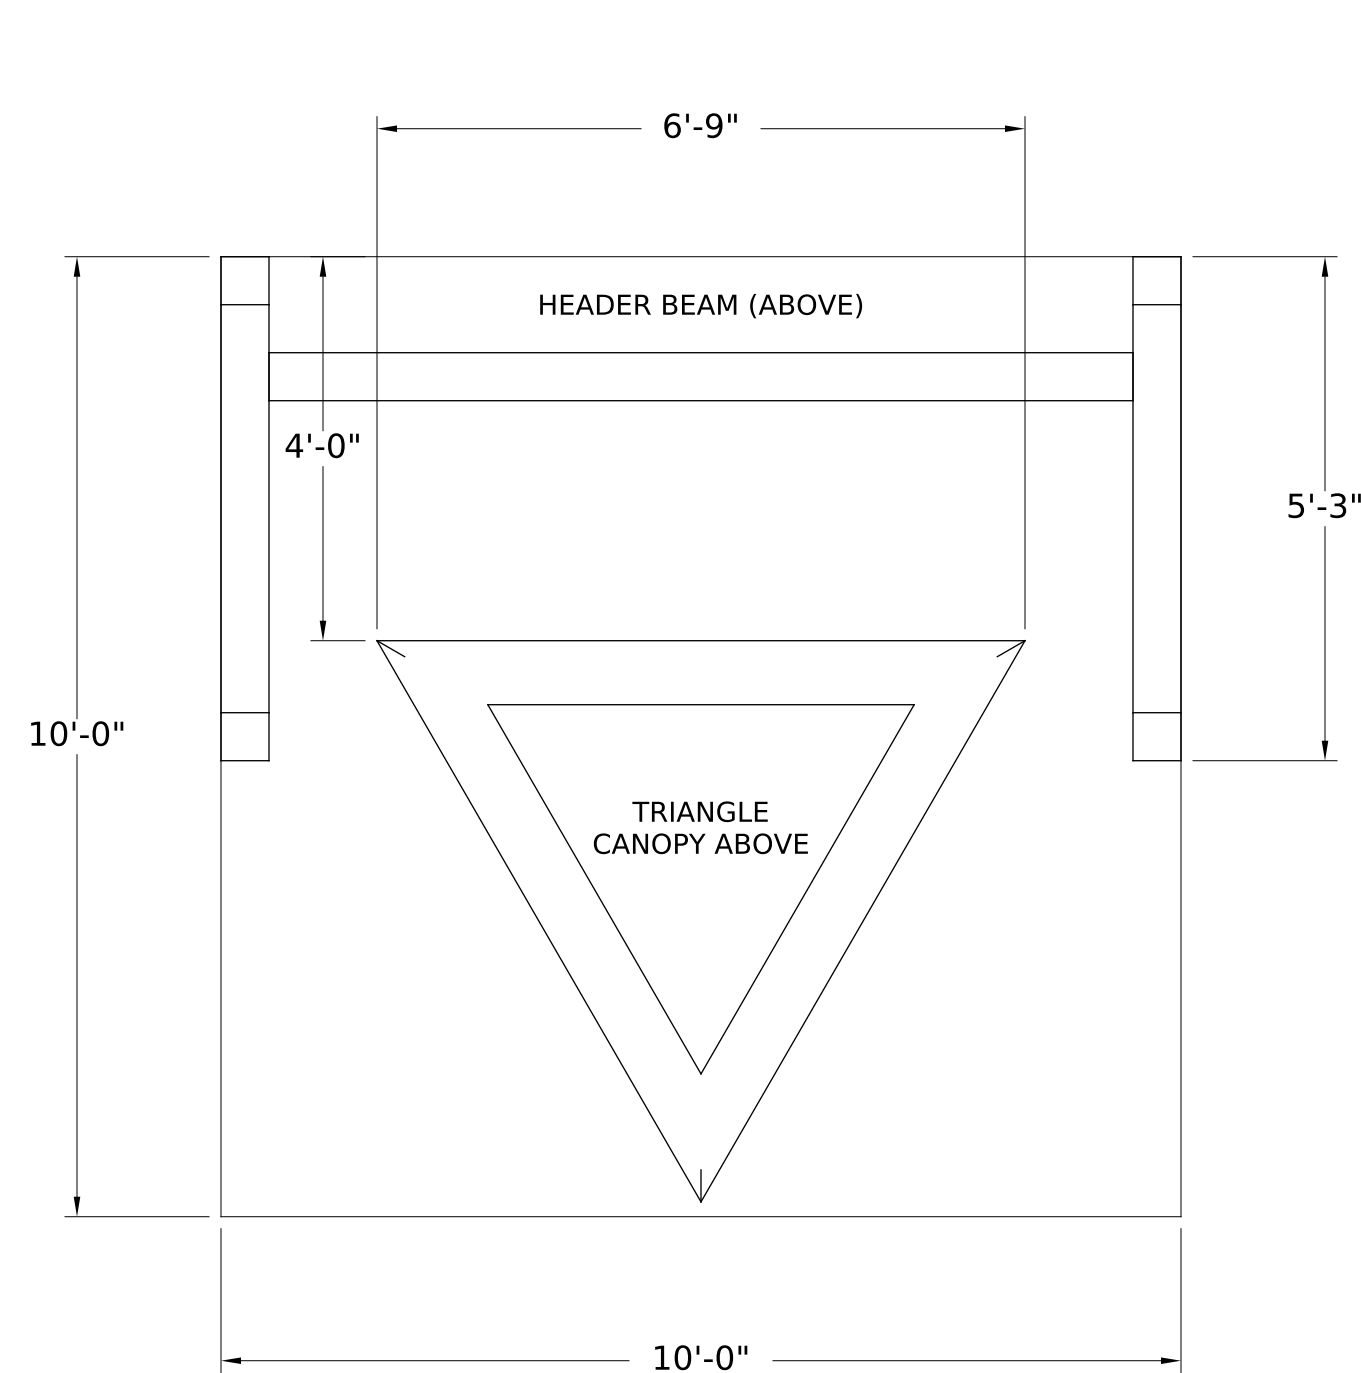


PLAN VIEW
SCALE: 1/2" = 1'-0"

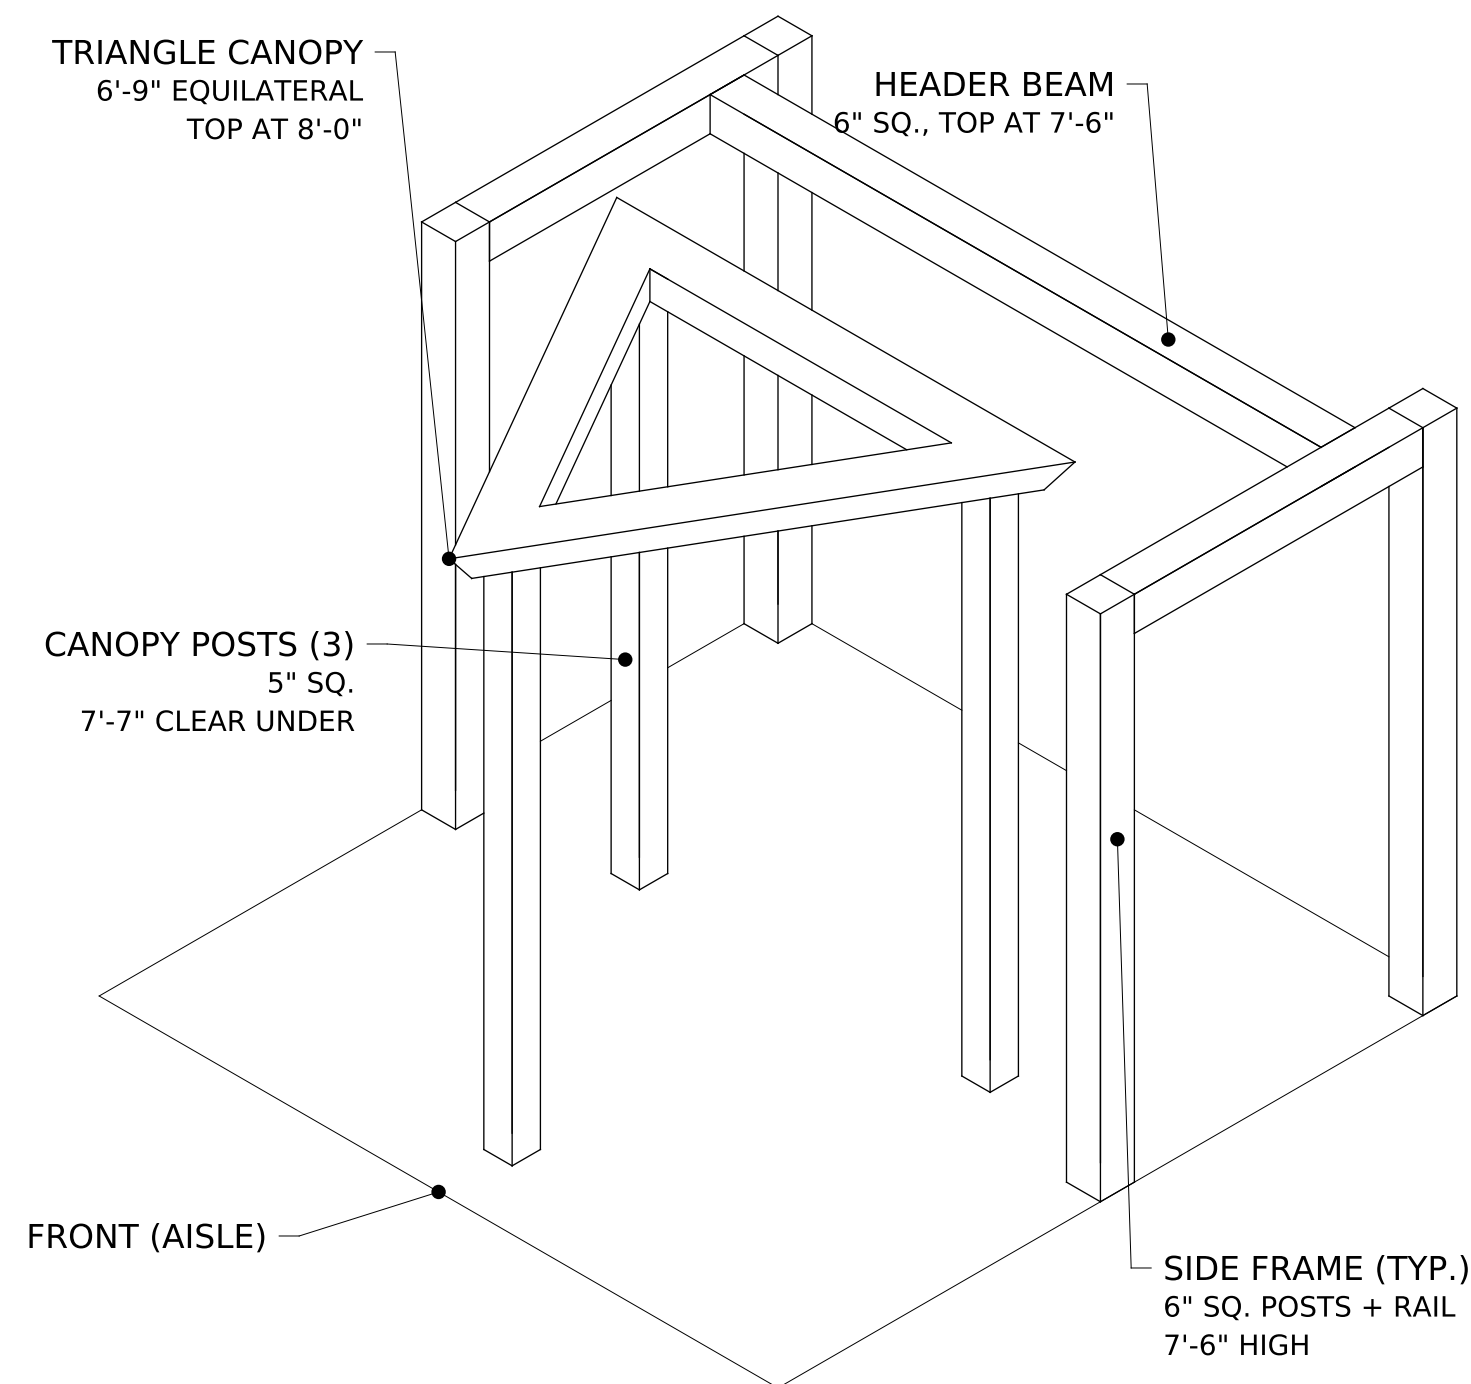

ISOMETRIC VIEW
NOT TO SCALE

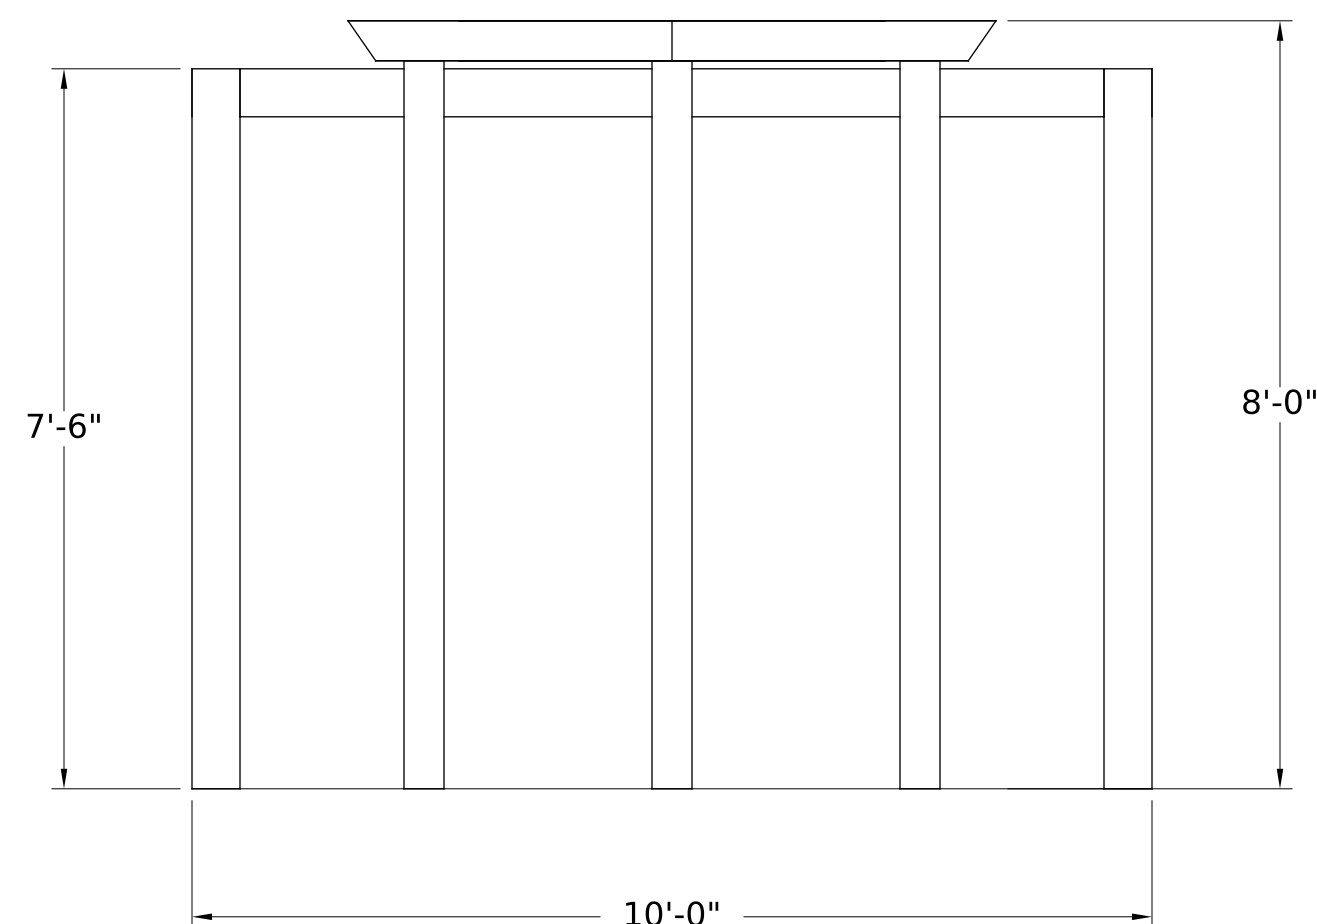

FRONT ELEVATION
SCALE: 1/2" = 1'-0"

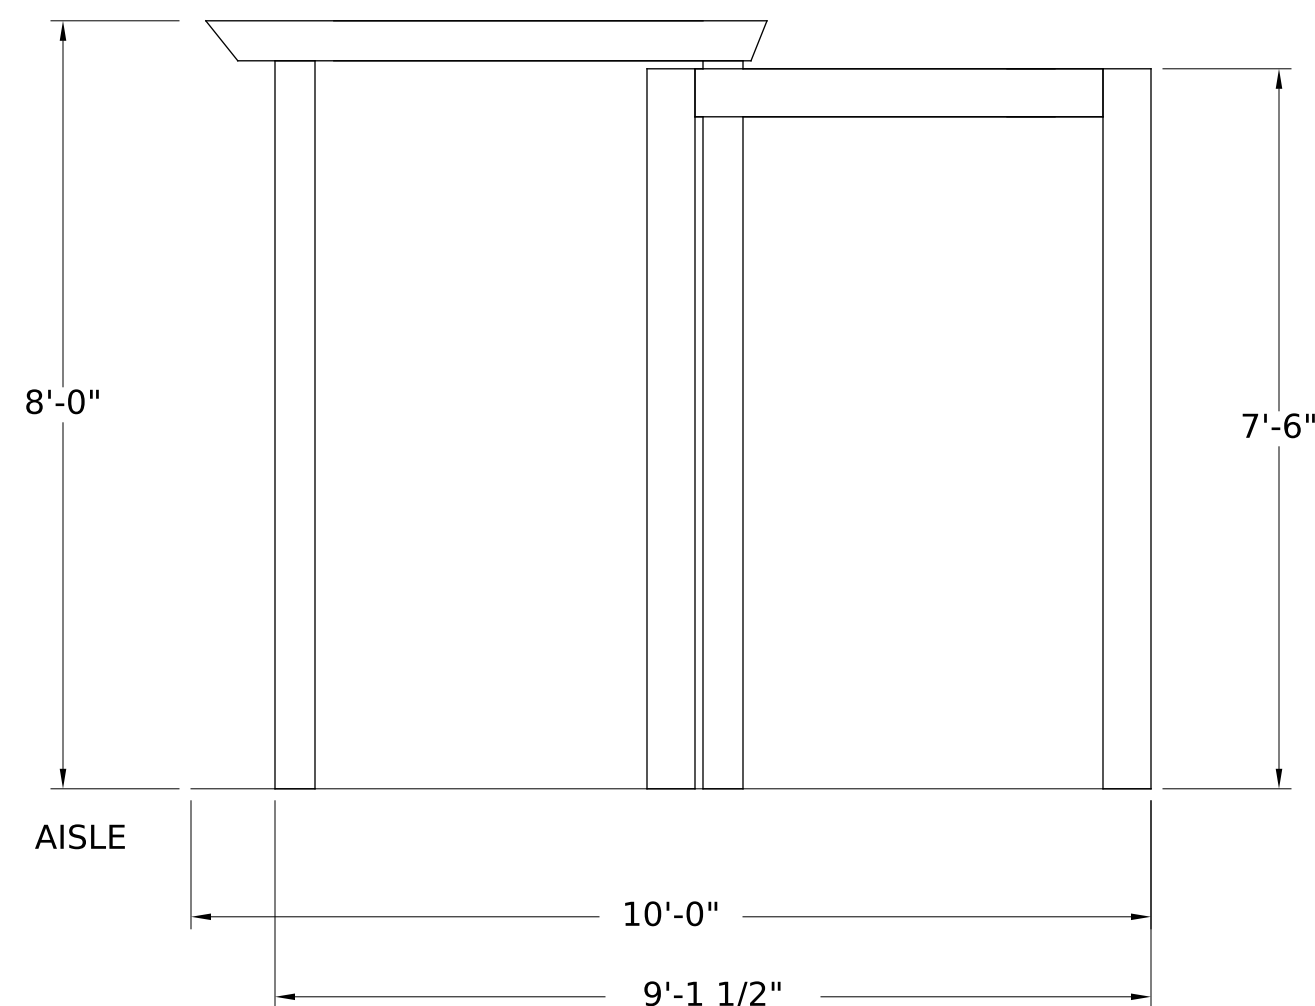

SIDE ELEVATION
SCALE: 1/2" = 1'-0"